
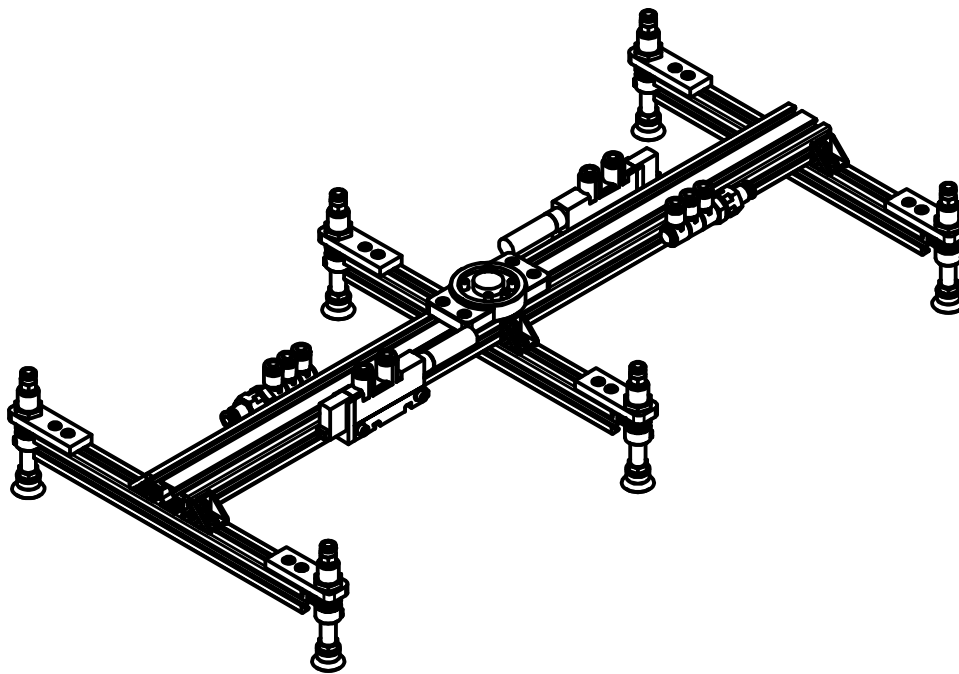
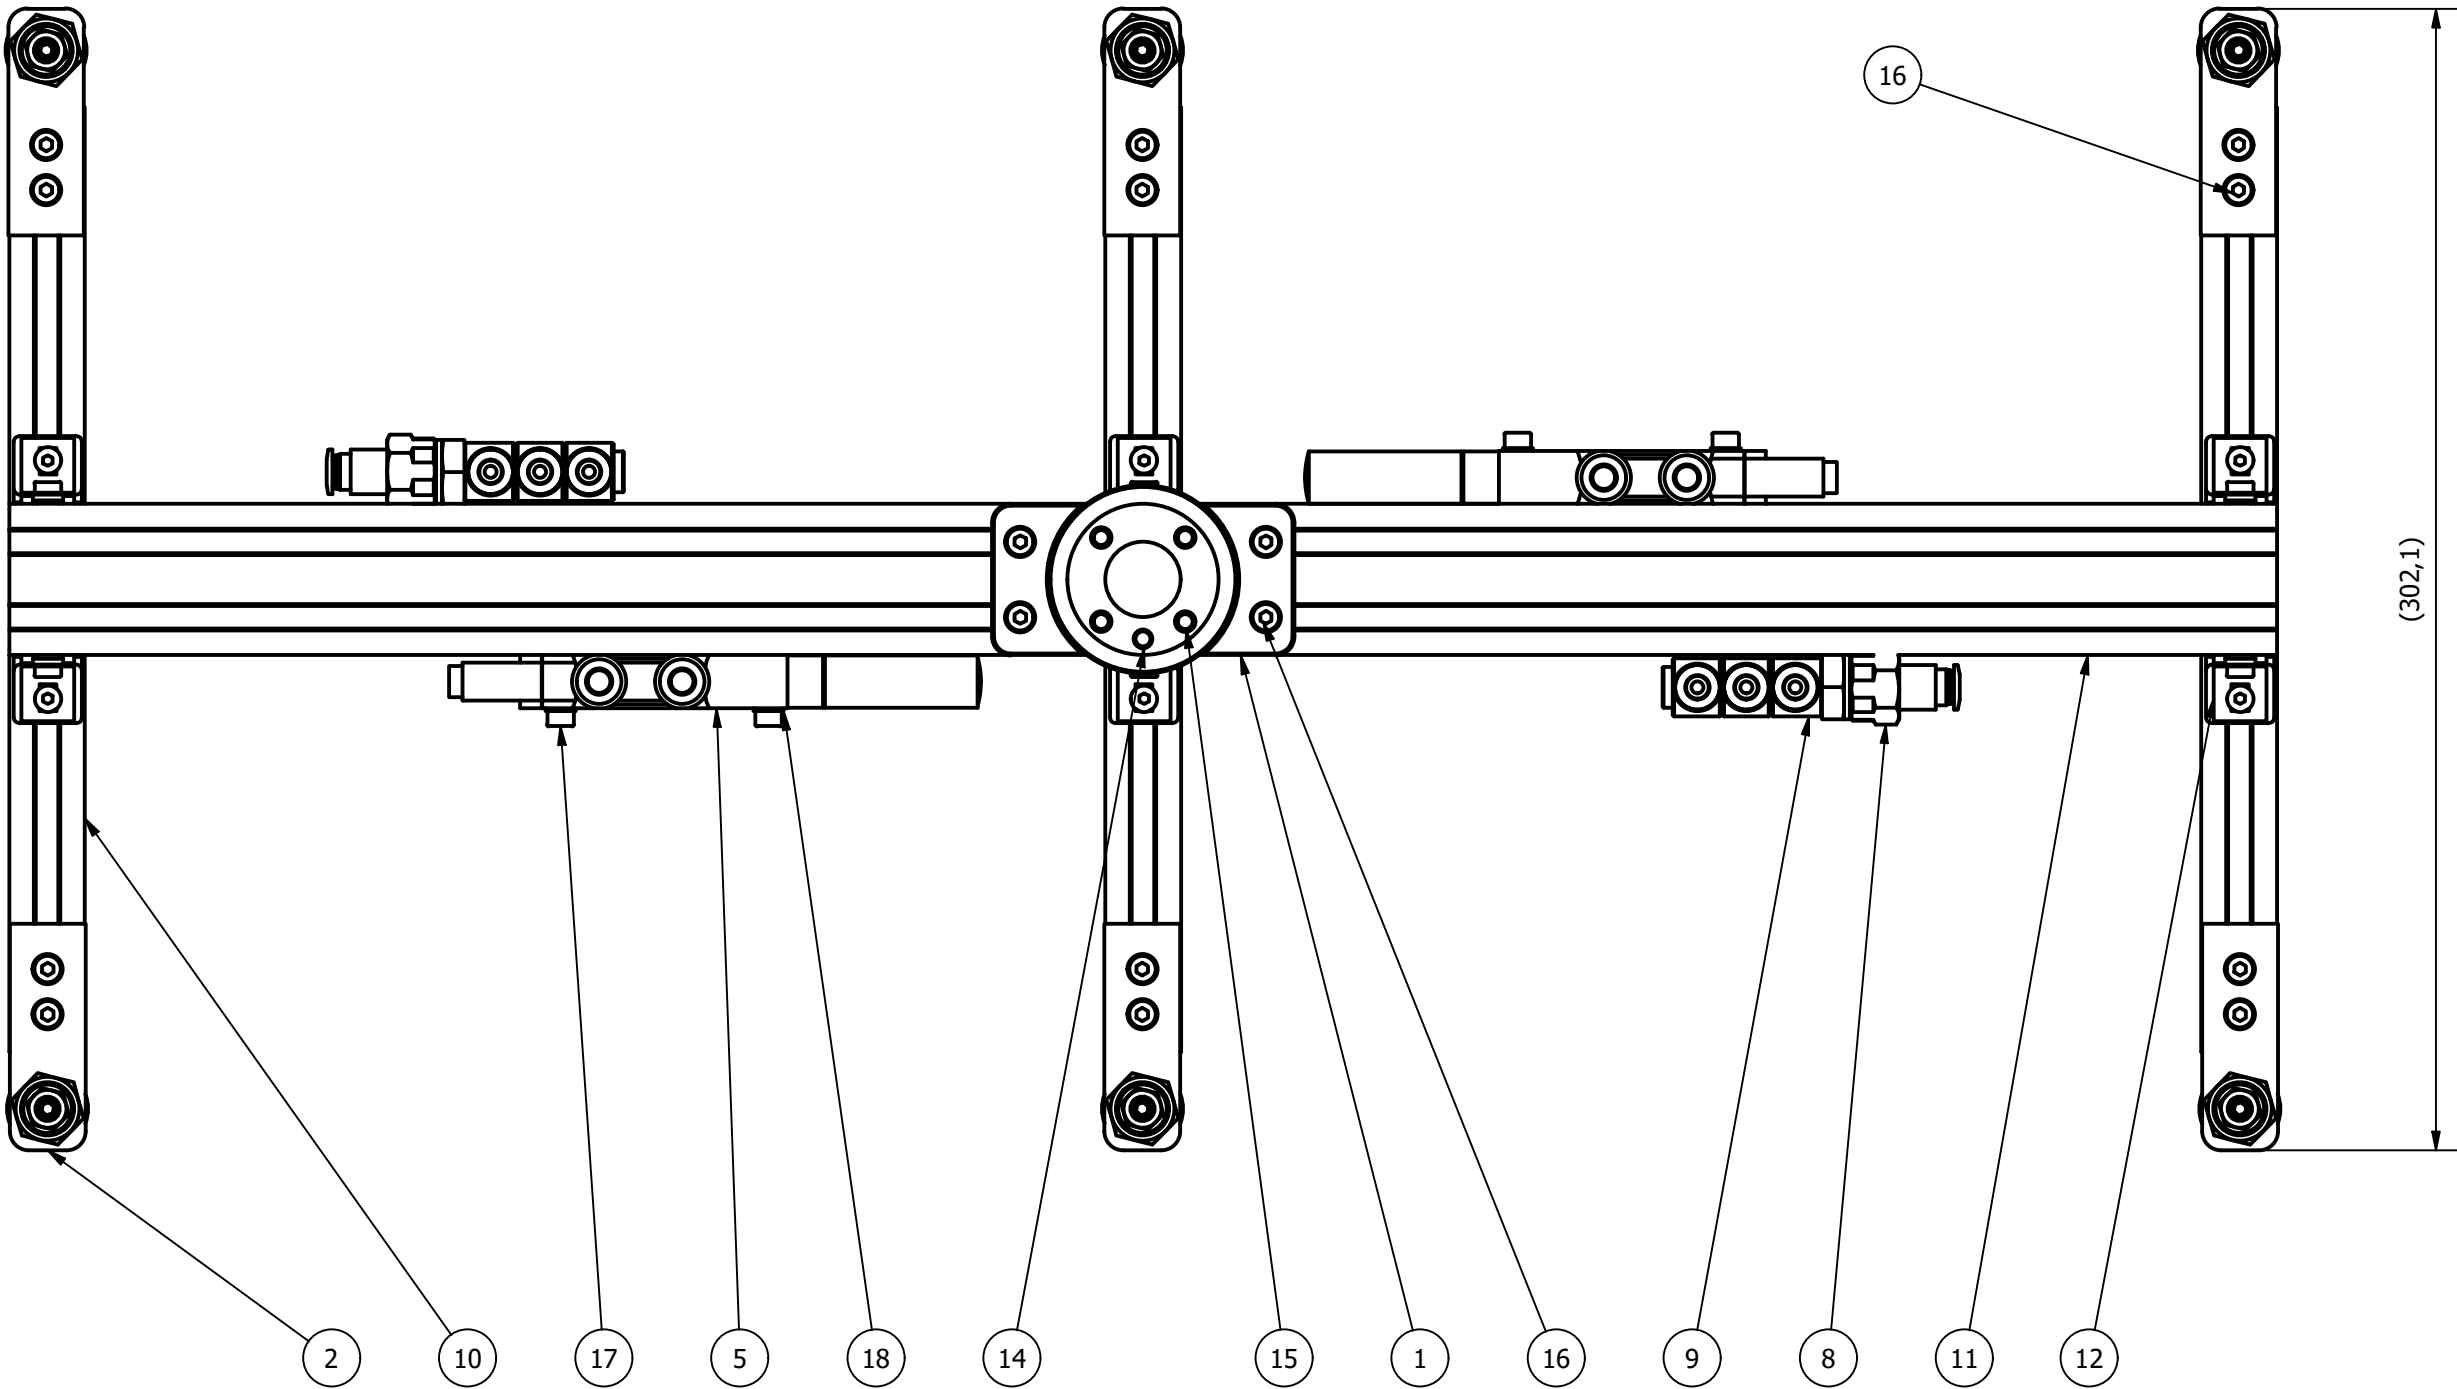
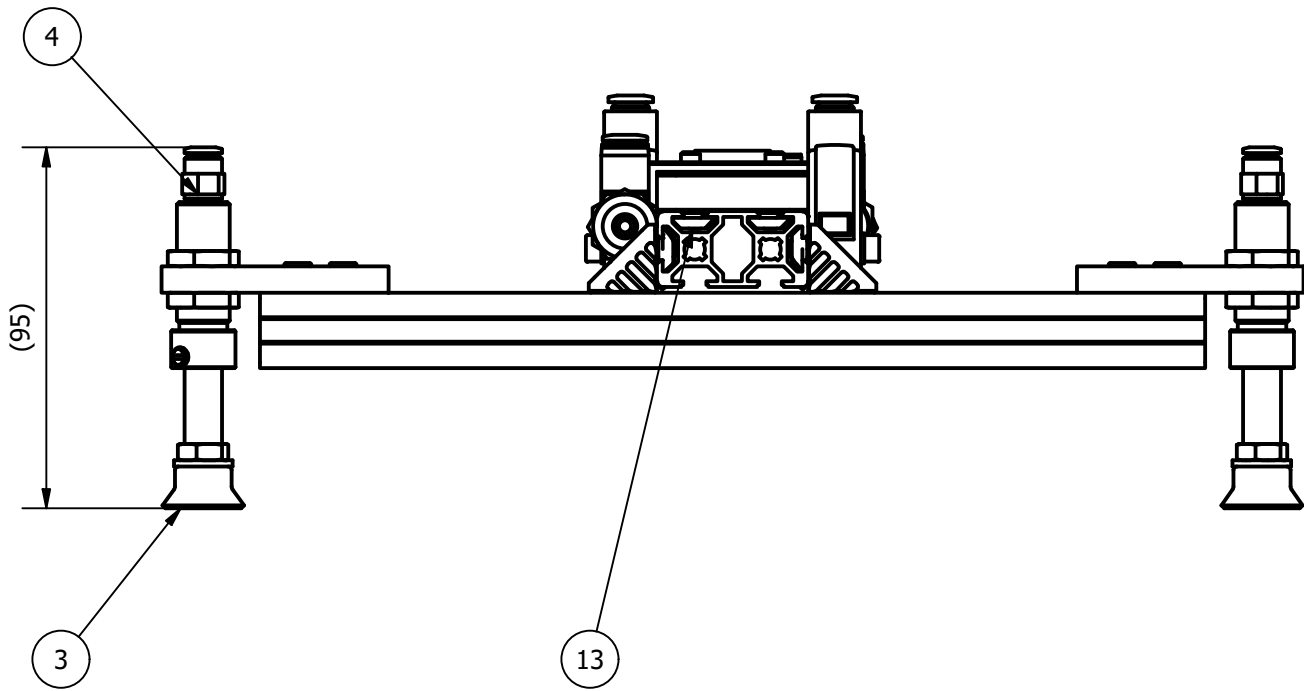


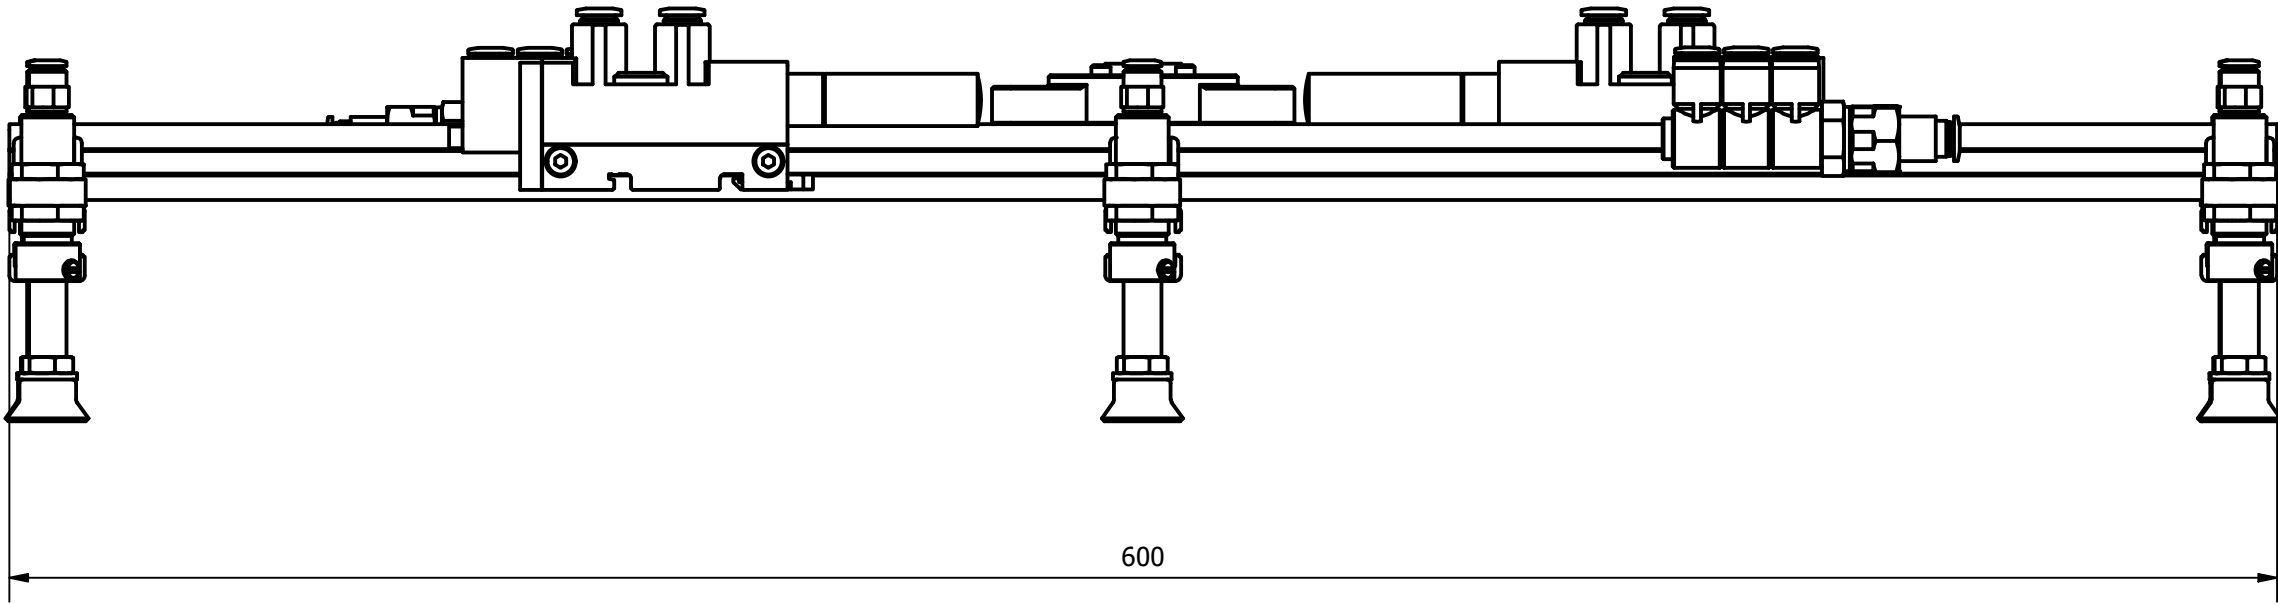

19	PRZEWODY PNEUMATYCZNE	—	PEN-6X1-BL	—	—	—	
18	PODKŁADKA	4	ISO 8738 4	STAL WĘGLOWA	—	—	
17	SRUBA M5x20	4	DIN EN ISO 4762	STAL 440C	—	—	
16	SRUBA M4x10	16	DIN EN ISO 4762	STAL 440C	—	—	
15	SRUBA M5x10	4	DIN EN ISO 4762	STAL 440C	—	—	
14	KOLEK USTALAJACY 5x10	1	DIN EN ISO 13337	AISI 321	—	—	
13	NAKRETKA MŁOTECZKOWA 10 M4	20	3842530281	STAL OCYNK	—	—	
12	KATOWNIK 20x20 SET	6	3842523511	ALUMINIUM	—	—	
11	PROFIL 20x40	1	3842992891	ALUMINIUM	—	—	
10	PROFIL 20x20	3	3842992888	ALUMINIUM	—	—	
9	ROZDZIELACZ WIELOSEGMENTOWY	2	QSLV3-G1/4-6	—	—	—	
8	ZŁACZKI WTYKOWE	2	QSF-1/4-6-B	—	—	—	
7	ZAWORY ZWROTNE	2	H-QS-6	—	—	—	
6	CZUJNIK CIŚNIENIA	2	SDE-5-VI-01 -Q6-P-M8	—	—	—	
5	GENERATOR PODCIŚNIENIA	2	VN-07-L-T3-PQ2 -VQ2-R01-M	—	—	—	
4	UCHWYTY	6	ESH-HCL-4-QS	—	—	—	
3	PRZYSŁAWKI	6	ESS-20-EU	—	—	—	
2	ADAPTER DO UCHWYTU	6	02.01.00	ALUMINIUM	—	—	
1	ELEMENT MOCUJACY CHWYTAKA	1	02.00.00	ALUMINIUM	—	—	
NR POZ.	NAZWA		L-BA SZTUK	NR RYSUNKU/NORMY	MATERIAL	MASA	UWAGI
KONSTRUOWAŁ		K.KOLANO		AGH	WYDZIAŁ IMIR		
SPRAWDZIŁ		J. BEDNARZ					
PODZIAŁKA	NAZWA			MATERIAL	MASA	NR RYSUNKU	
1 : 2	CH. PODCIŚNIENIOWY			—	—	02.00.01	